Esquema de trazado de la maqueta (tabla 1100 × 800 mm) — medidas en mm desde la esquina superior izquierda

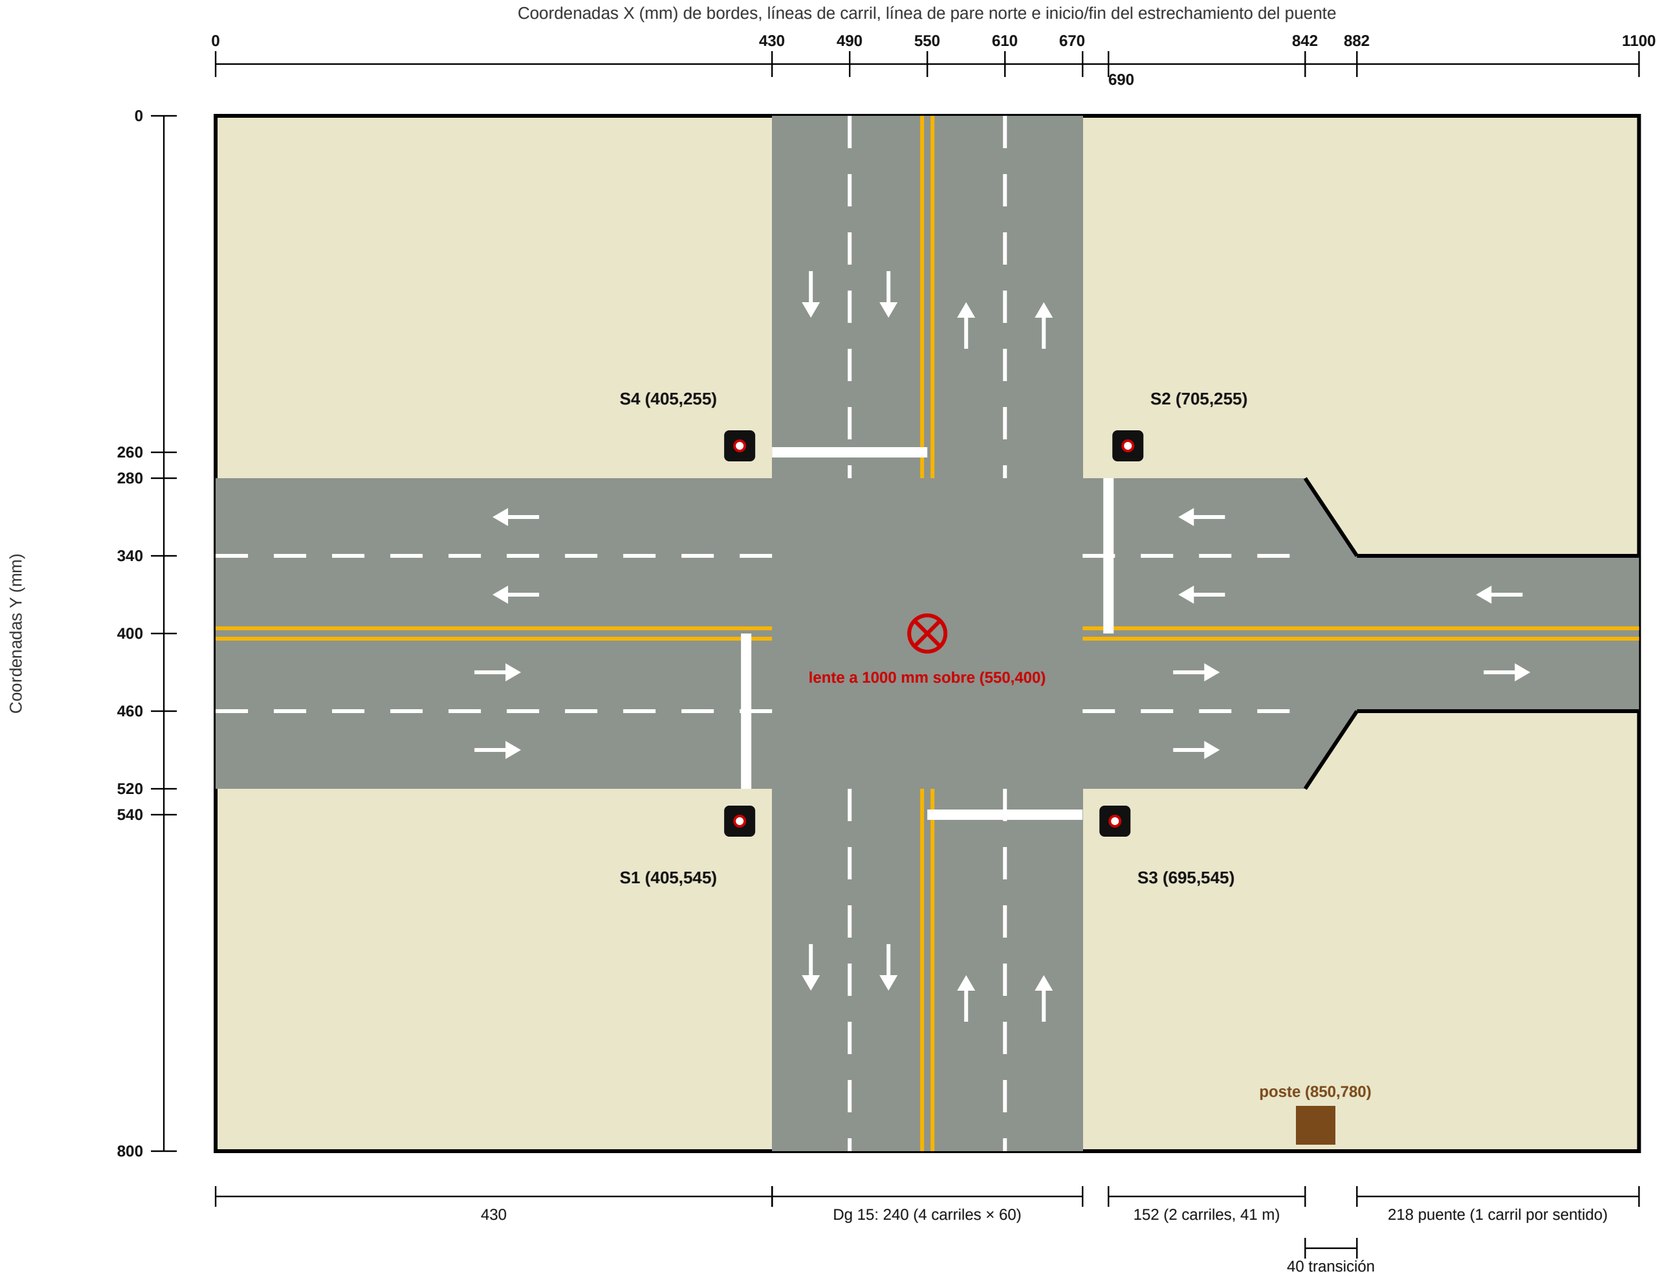

Referencia de trazado

CALZADA

Cra 23 (horizontal): y = 280 a 520, de x = 0 a 1100
excepto puente: desde x = 882, solo y = 340 a 460
transición 842→882: diagonal (842,280)–(882,340)
y (842,520)–(882,460)
Dg 15 (vertical): x = 430 a 670, de y = 0 a 800

CARRILES: 60 mm (4 por calle; puente 2)

Cra 23: blanca discontinua en y = 340 y y = 460
de x = 0 a 430 y de x = 670 a 842 (no en el puente)
Dg 15: blanca discontinua en x = 490 y x = 610
de y = 0 a 280 y de y = 520 a 800
Discontinua: 25 mm de línea + 20 mm de espacio

LÍNEA CENTRAL doble amarilla continua

Cra 23: y = 396 y y = 404 (x 0–430 y 670–1100)
Dg 15: x = 546 y x = 554 (y 0–280 y 520–800)
No se pinta nada dentro del cruce (430–670 × 280–520)

LÍNEAS DE PARE: blancas, 8 mm de ancho

Norte (Cra 23, derecha): x = 690, de y = 280 a 400
Sur (Cra 23, izquierda): x = 410, de y = 400 a 520
Este (Dg 15, arriba): y = 260, de x = 430 a 550
Oeste (Dg 15, abajo): y = 540, de x = 550 a 670

SEMÁFOROS: poste hueco de ~80 mm sobre hueco Ø8

(centro del poste = centro del hueco; LED de frente al carril)
S1 Cra 23 sur: (405,545) · LED miran a la izquierda
S2 Cra 23 norte: (705,255) · LED miran a la derecha
S3 Dg 15 oeste: (695,545) · LED miran hacia abajo
S4 Dg 15 este: (405,255) · LED miran hacia arriba
Cables por dentro del poste hasta el ESP32 (debajo)

CÁMARA

Poste en (850,780); lente a 1000 mm sobre (550,400)
Imagen horizontal, lado largo paralelo a la Cra 23

COLORES (todo MATE; RAL = referencia, sirve equivalente)

Calzada: gris medio tipo asfalto, RAL 7042 (gris tráfico A)
NO gris muy oscuro: los carros negros/azules se pierden
Aceras y resto de la tabla: hueso/beige claro, RAL 1013
Carriles, pare: blanco, RAL 9016 (blanco tráfico)
Línea central: amarillo, RAL 1023 (amarillo tráfico)
Postes de semáforo: negro mate, RAL 9005
Bordes del puente: línea negra o gris oscuro, 3–5 mm

NOTAS

Las flechas blancas del dibujo NO se pintan.
Sin texto ni dibujos sobre la tabla. Sin barniz brillante.
Tránsito por la derecha. Medir siempre desde la
esquina superior izquierda (lado de 1100 arriba).