Plano de la tabla de la maqueta con el PUENTE (cuello de botella) — escala 1:10, mm

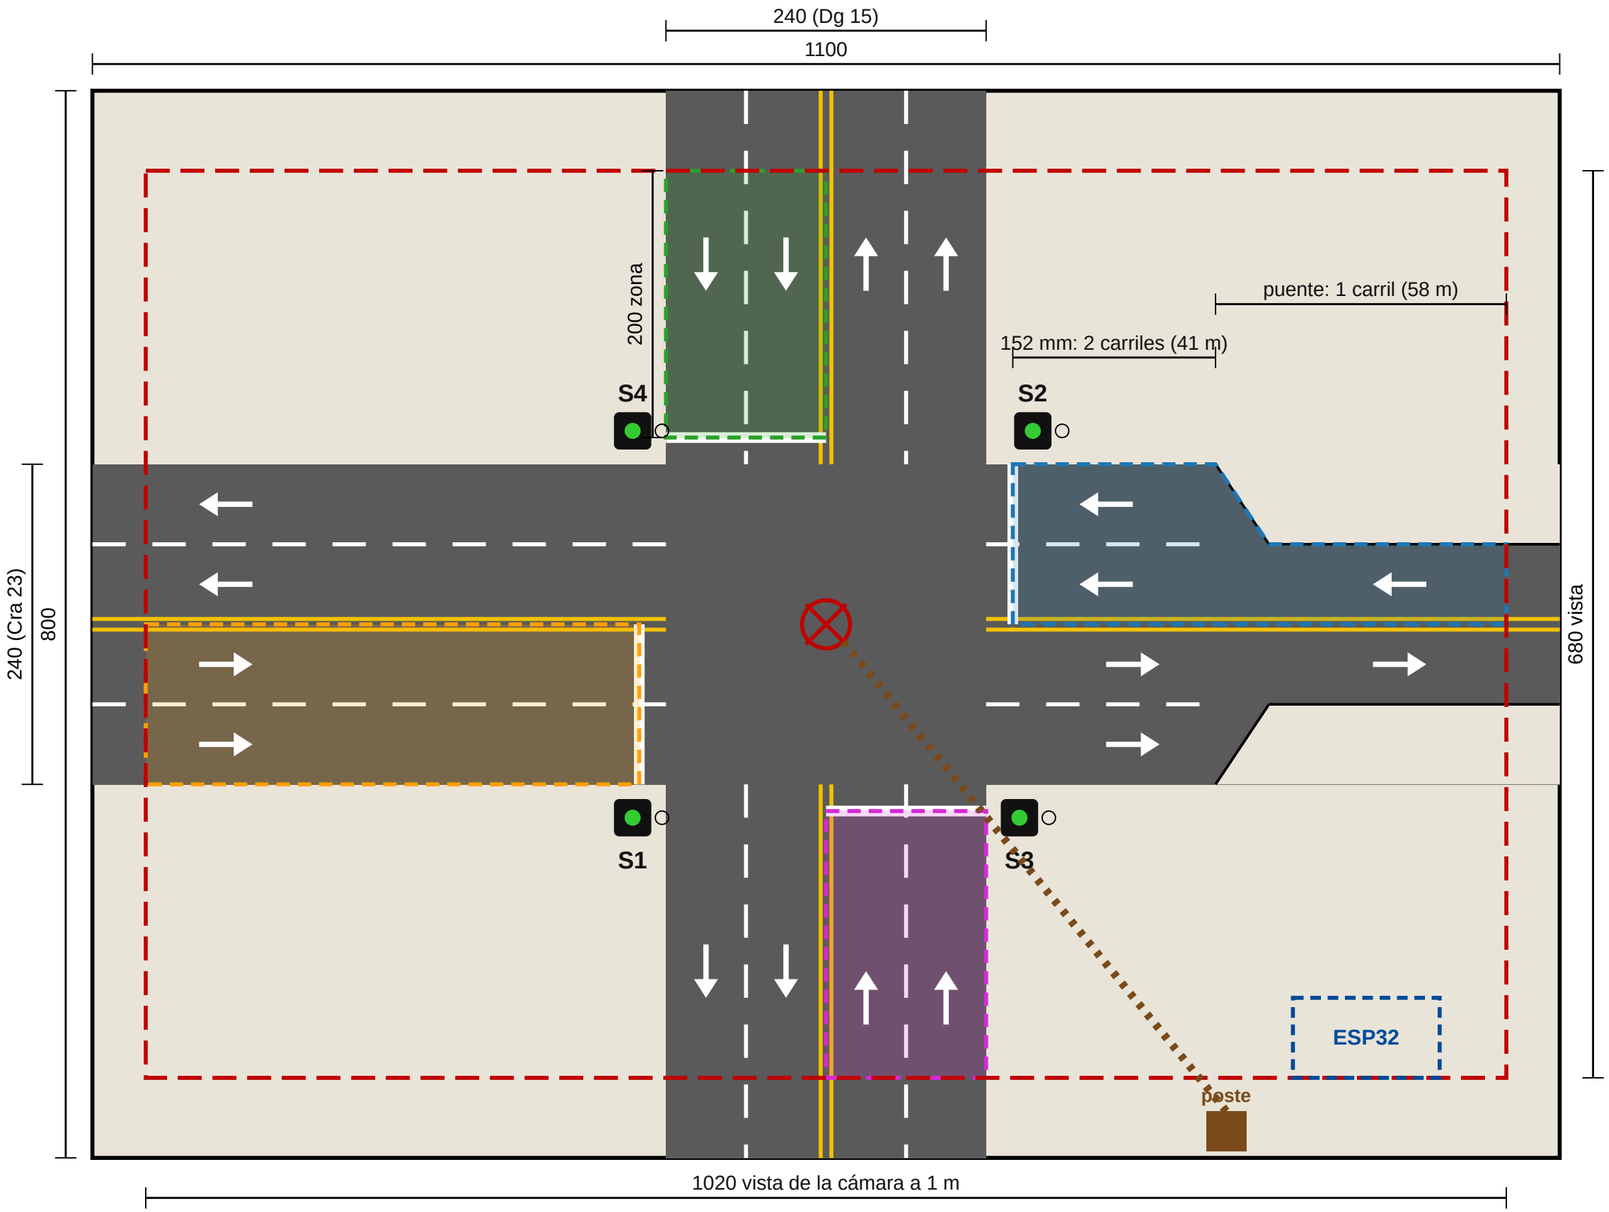

Convenciones

- Calzada: pintura gris oscuro MATE
- Carril 60 mm (4 por calle), discontinua blanca
- Línea central doble amarilla
- Línea de pare: 20 mm antes del cruce
- Lo que ve la cámara a 1 m (102 × 68 cm medido)
- Zonas de conteo por brazo (solo software, NO se pintan)
- Semáforo (módulo LED) + hueco Ø8 mm para cables
- ESP32 + protoboard DEBAJO de la tabla
- Poste de la cámara en la acera (borde inferior, fuera de la vista); brazo en diagonal hasta el centro, lente a 1 m sobre la tabla

Semáforos (hardware/esp32/conexiones.md)

S1 Cra 23 sur: D32 / D33 / D25
S2 Cra 23 norte: D26 / D27 / D13
S3 Dg 15 oeste: D23 / D22 / D21
S4 Dg 15 este: D19 / D18 / D17

Notas

Tránsito por la derecha (Colombia).
2 carriles de llegada por brazo, como la red SUMO.
Capacidad estimada por brazo: Cra 23 ≈ 8 carros,
Dg 15 ≈ 4 (Hot Wheels de 7 cm + 1,5 cm).
SIN texto ni dibujos en la tabla (falsos positivos).
Acabado mate (sin barniz brillante).
Semáforos en las aceras, fuera de las zonas.
Poste: 60 mm de margen inferior, fuera de la vista.
Las calles llegan al borde: los carros entran
desde fuera de la vista.
Brazo norte: igual que la red SUMO (41 m de 2 carriles
+ puente de 1 carril por sentido, 58 m) a 3,7 mm/m.
Capacidad del brazo norte ≈ 4 carros.